
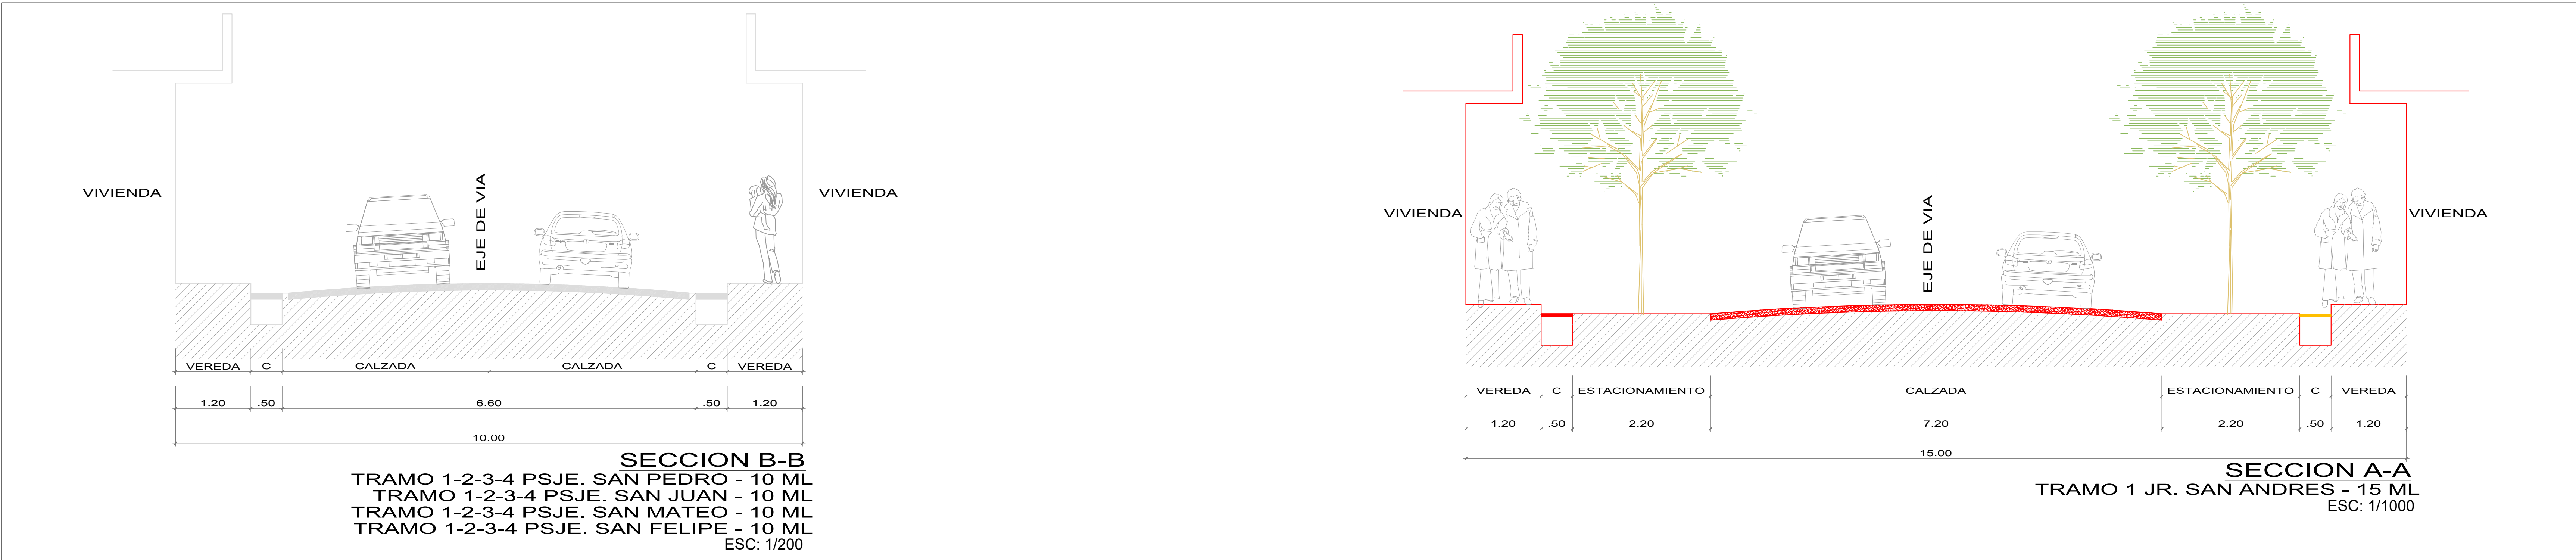


# HABILITACIÓN URBANA "MI BENDICIÓN" - SEGUNDA DE JERUSALEN

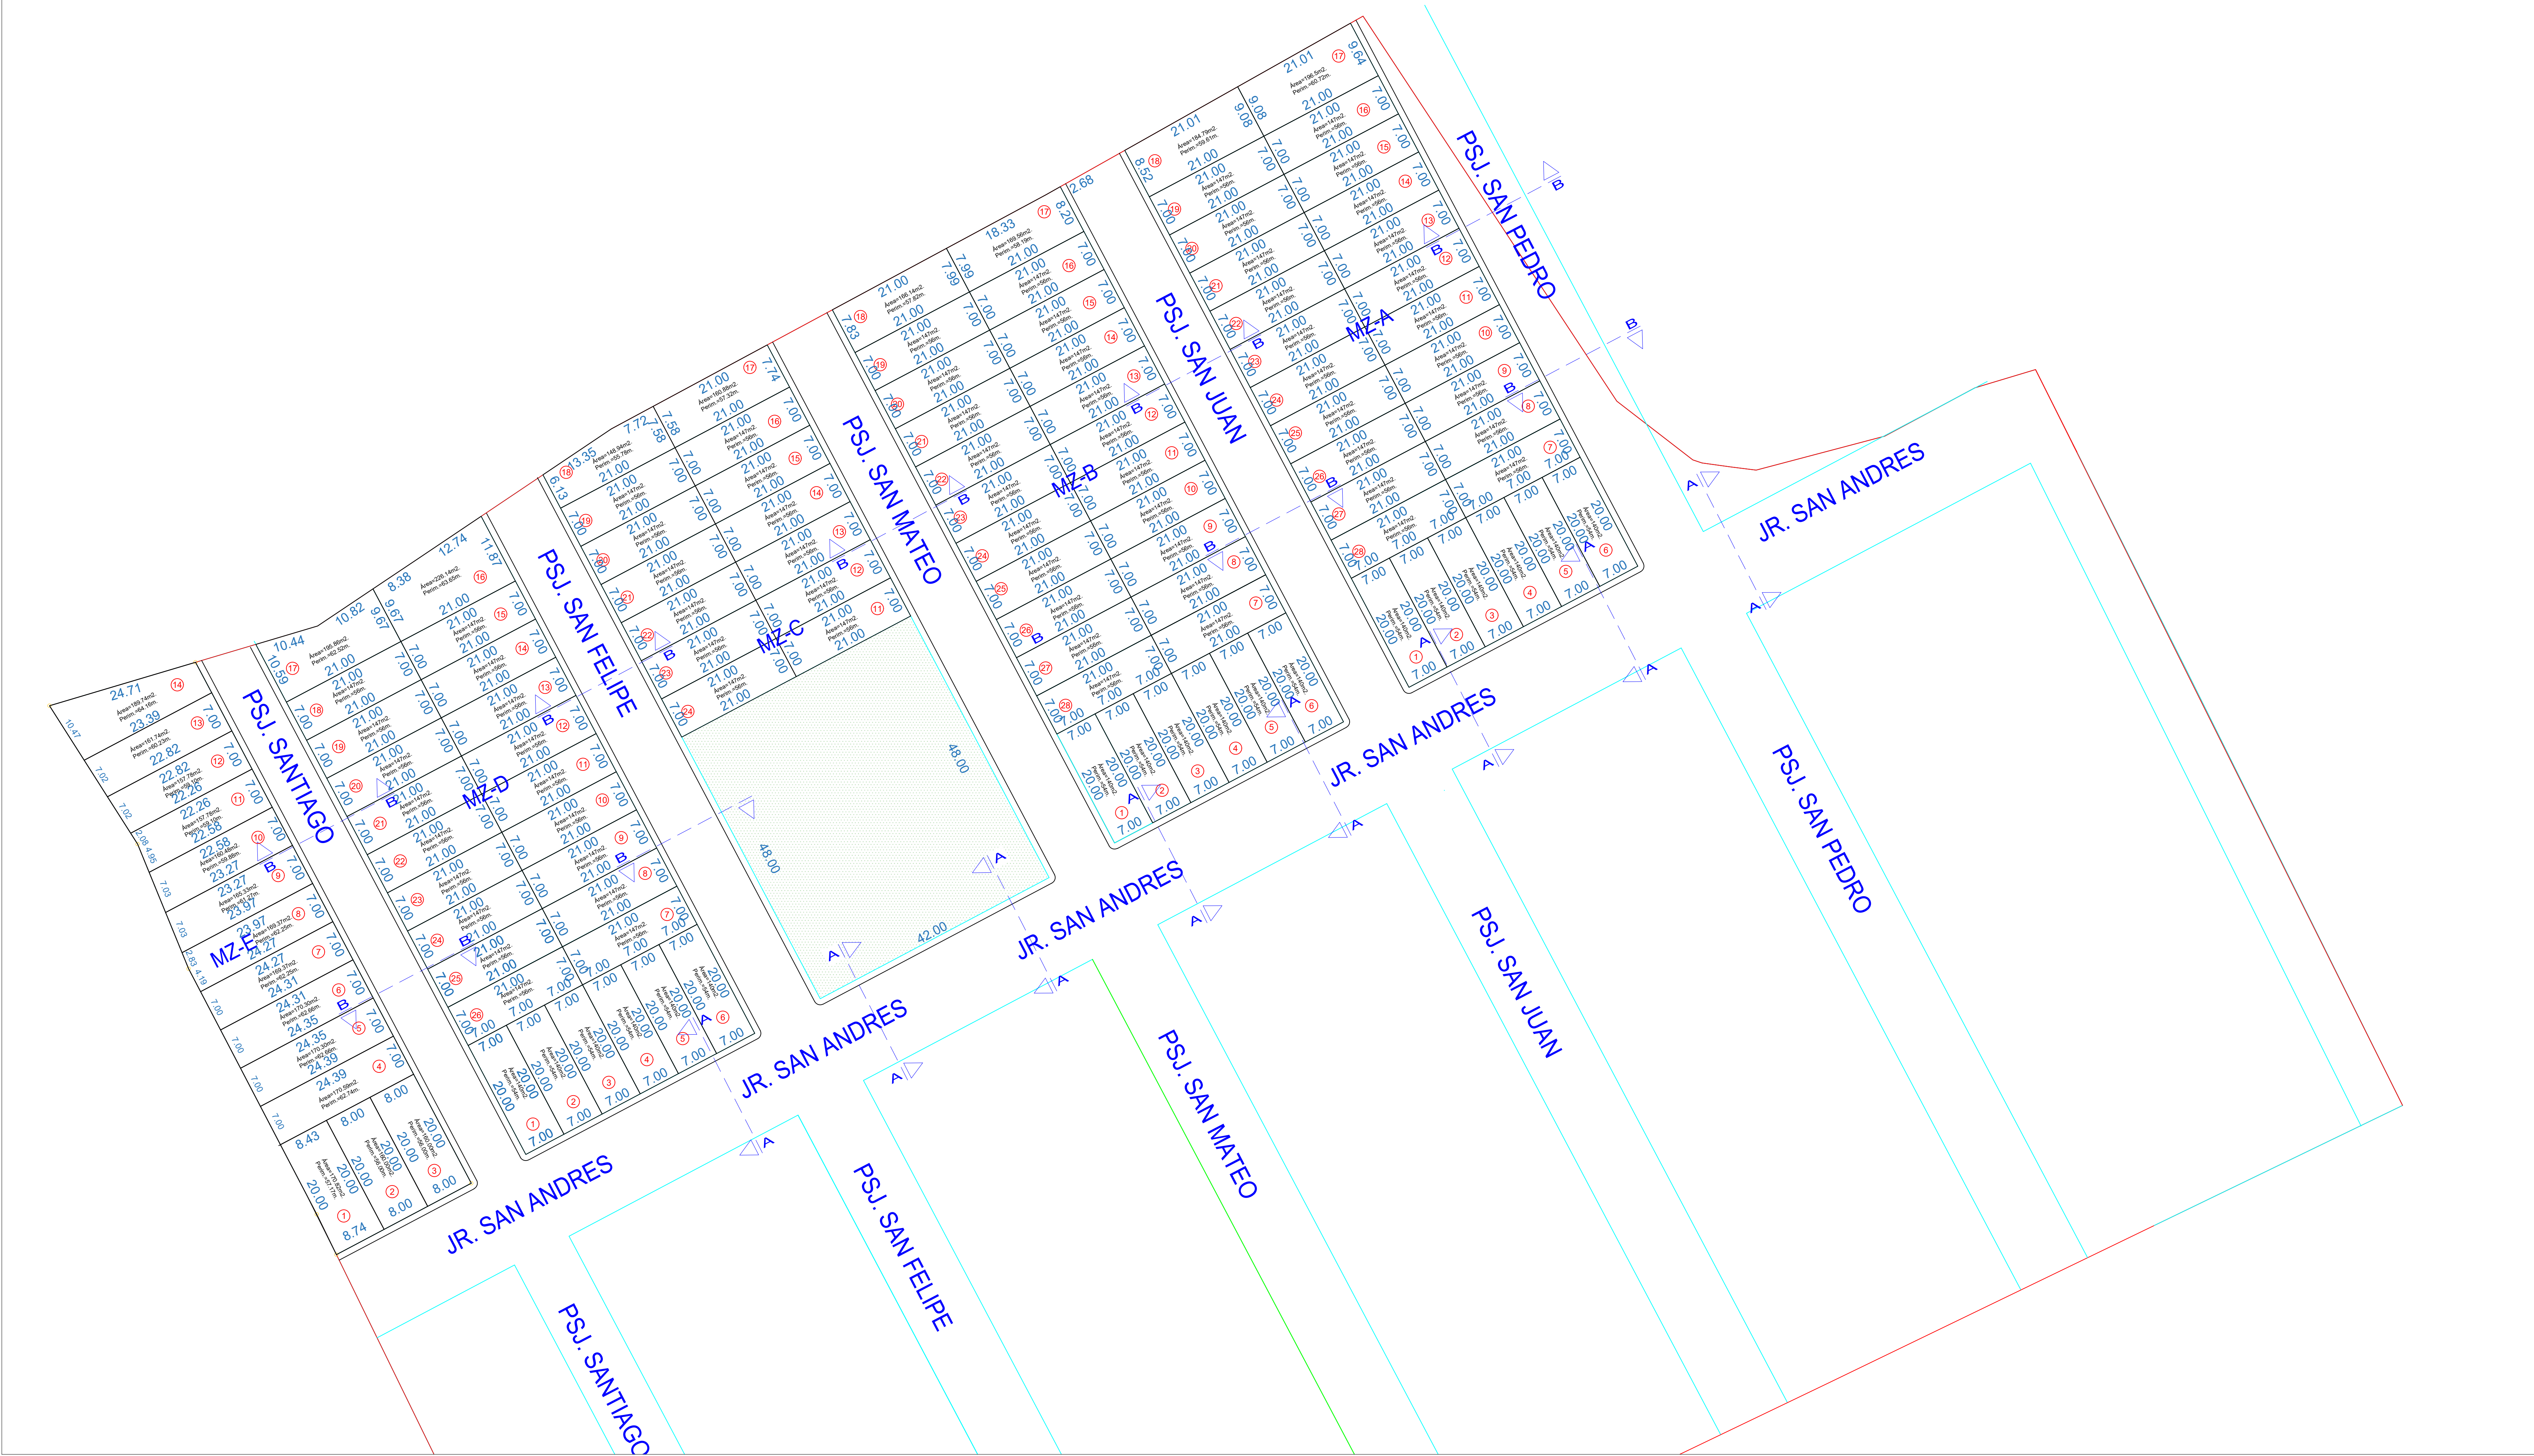

|                                          |  |   |  |
|------------------------------------------|--|---|--|
|                                          |  | PROYECTO:<br>HABILITACIÓN URBANA "MI BENDICIÓN"                                                                       |  |
| PLANOS:<br>PLANO DE TRAZADO Y LOTIZACIÓN |  | UBICACIÓN:<br>SECTOR VALLE GRANDE<br>SEGUNDA JERUSALEN - ELIAS SOPLIN VARGAS, PROVINCIA DE RIOJA<br>REGION SAN MARTIN |  |
| INSCRIPCIÓN REGISTRAL:<br>N° PARTIDA:    |  | ESCALA:<br>1/750   |  |
| PROPIETARIO:<br>FAMILIA TORRES           |  | FIRMA DEL PROFESIONAL RESPONSABLE:                                                                                    |  |
| SECTOR:<br>VALLE GRANDE                  |  | LÁMINA:<br>01   |  |
| DISTRITO:<br>ELIAS SOPLIN VARGAS         |  | PROVINCIA:<br>RIOJA                                                                                                   |  |
| REGION:<br>SAN MARTIN                    |  | FECHA:<br>14/07/2023                                                                                                  |  |