


HABILITACIÓN URBANA "VILLA CLUB -LAS FLORES"

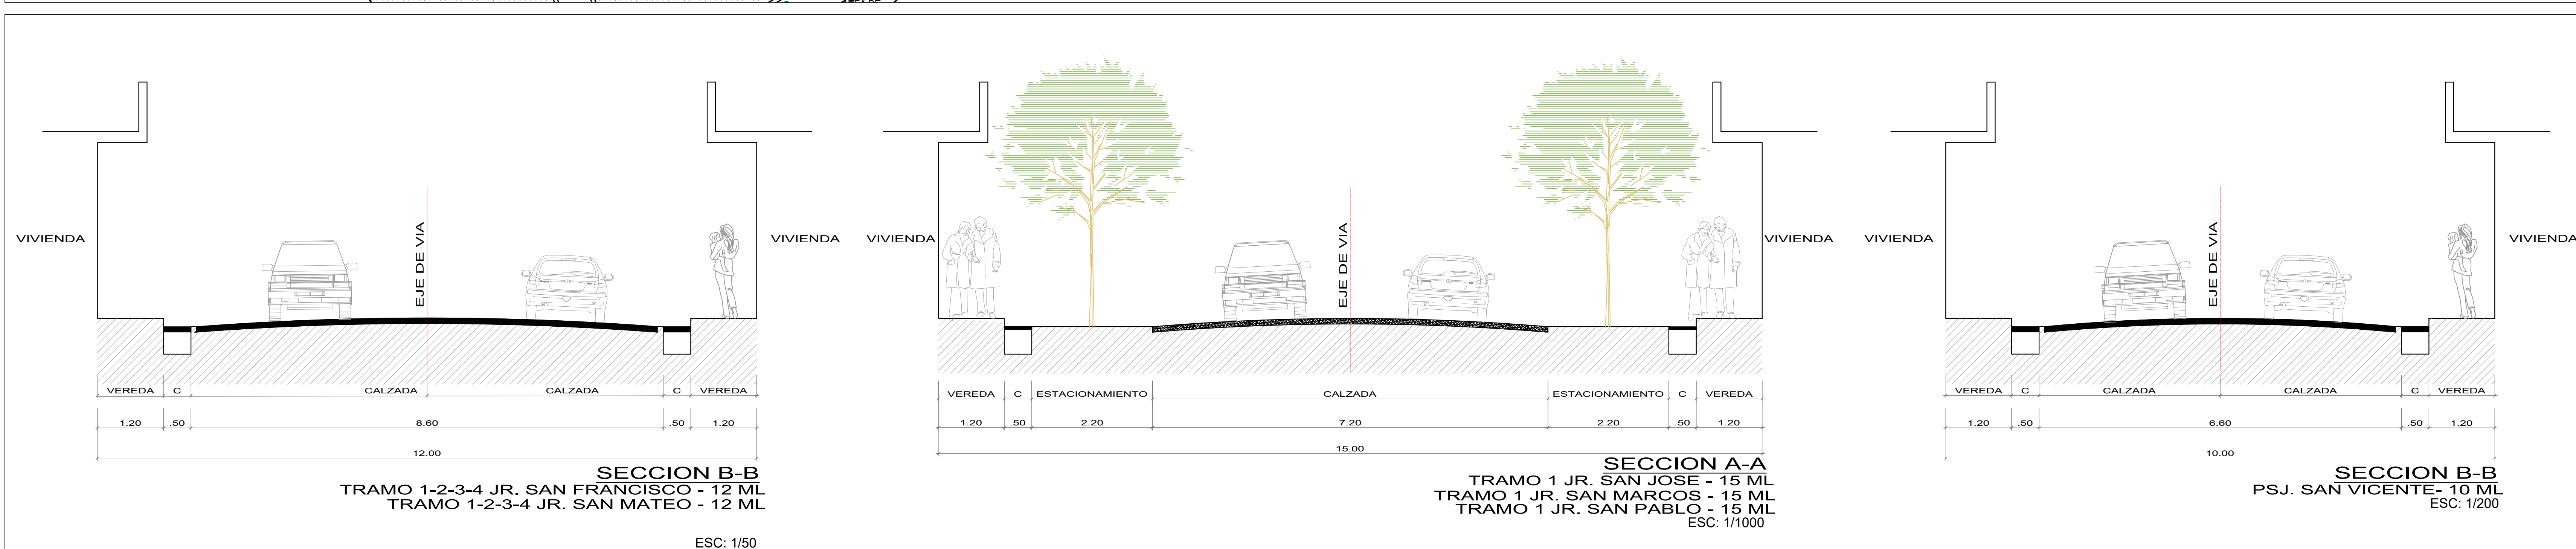

 FAN CONSTRUCTORES GENERALES	PROYECTO: HABITACION URBANA "YULA CILIA LAS FLORES" PLANO: PLANO DE TRAZADO Y LOTIZACION UBICACION: SECTOR JUAN VELASCO ALVARADO NUEVA CAJAMARCA, PROVINCIA DE RIOJA REGION SAN MARTIN INSCRIPCION REGISTRAL: N° PARTIDA: 11042627	ESCALA: 1/750
	PROPIETARIO: YULA CILIA LAS FLORES SOCIEDAD ANONIMA CERRADA SECTOR: JUAN VELASCO ALVARADO DISTRITO: NUEVA CAJAMARCA REGION: SAN MARTIN	PROVINCIA: RIOJA FECHA: 01/02/2023