


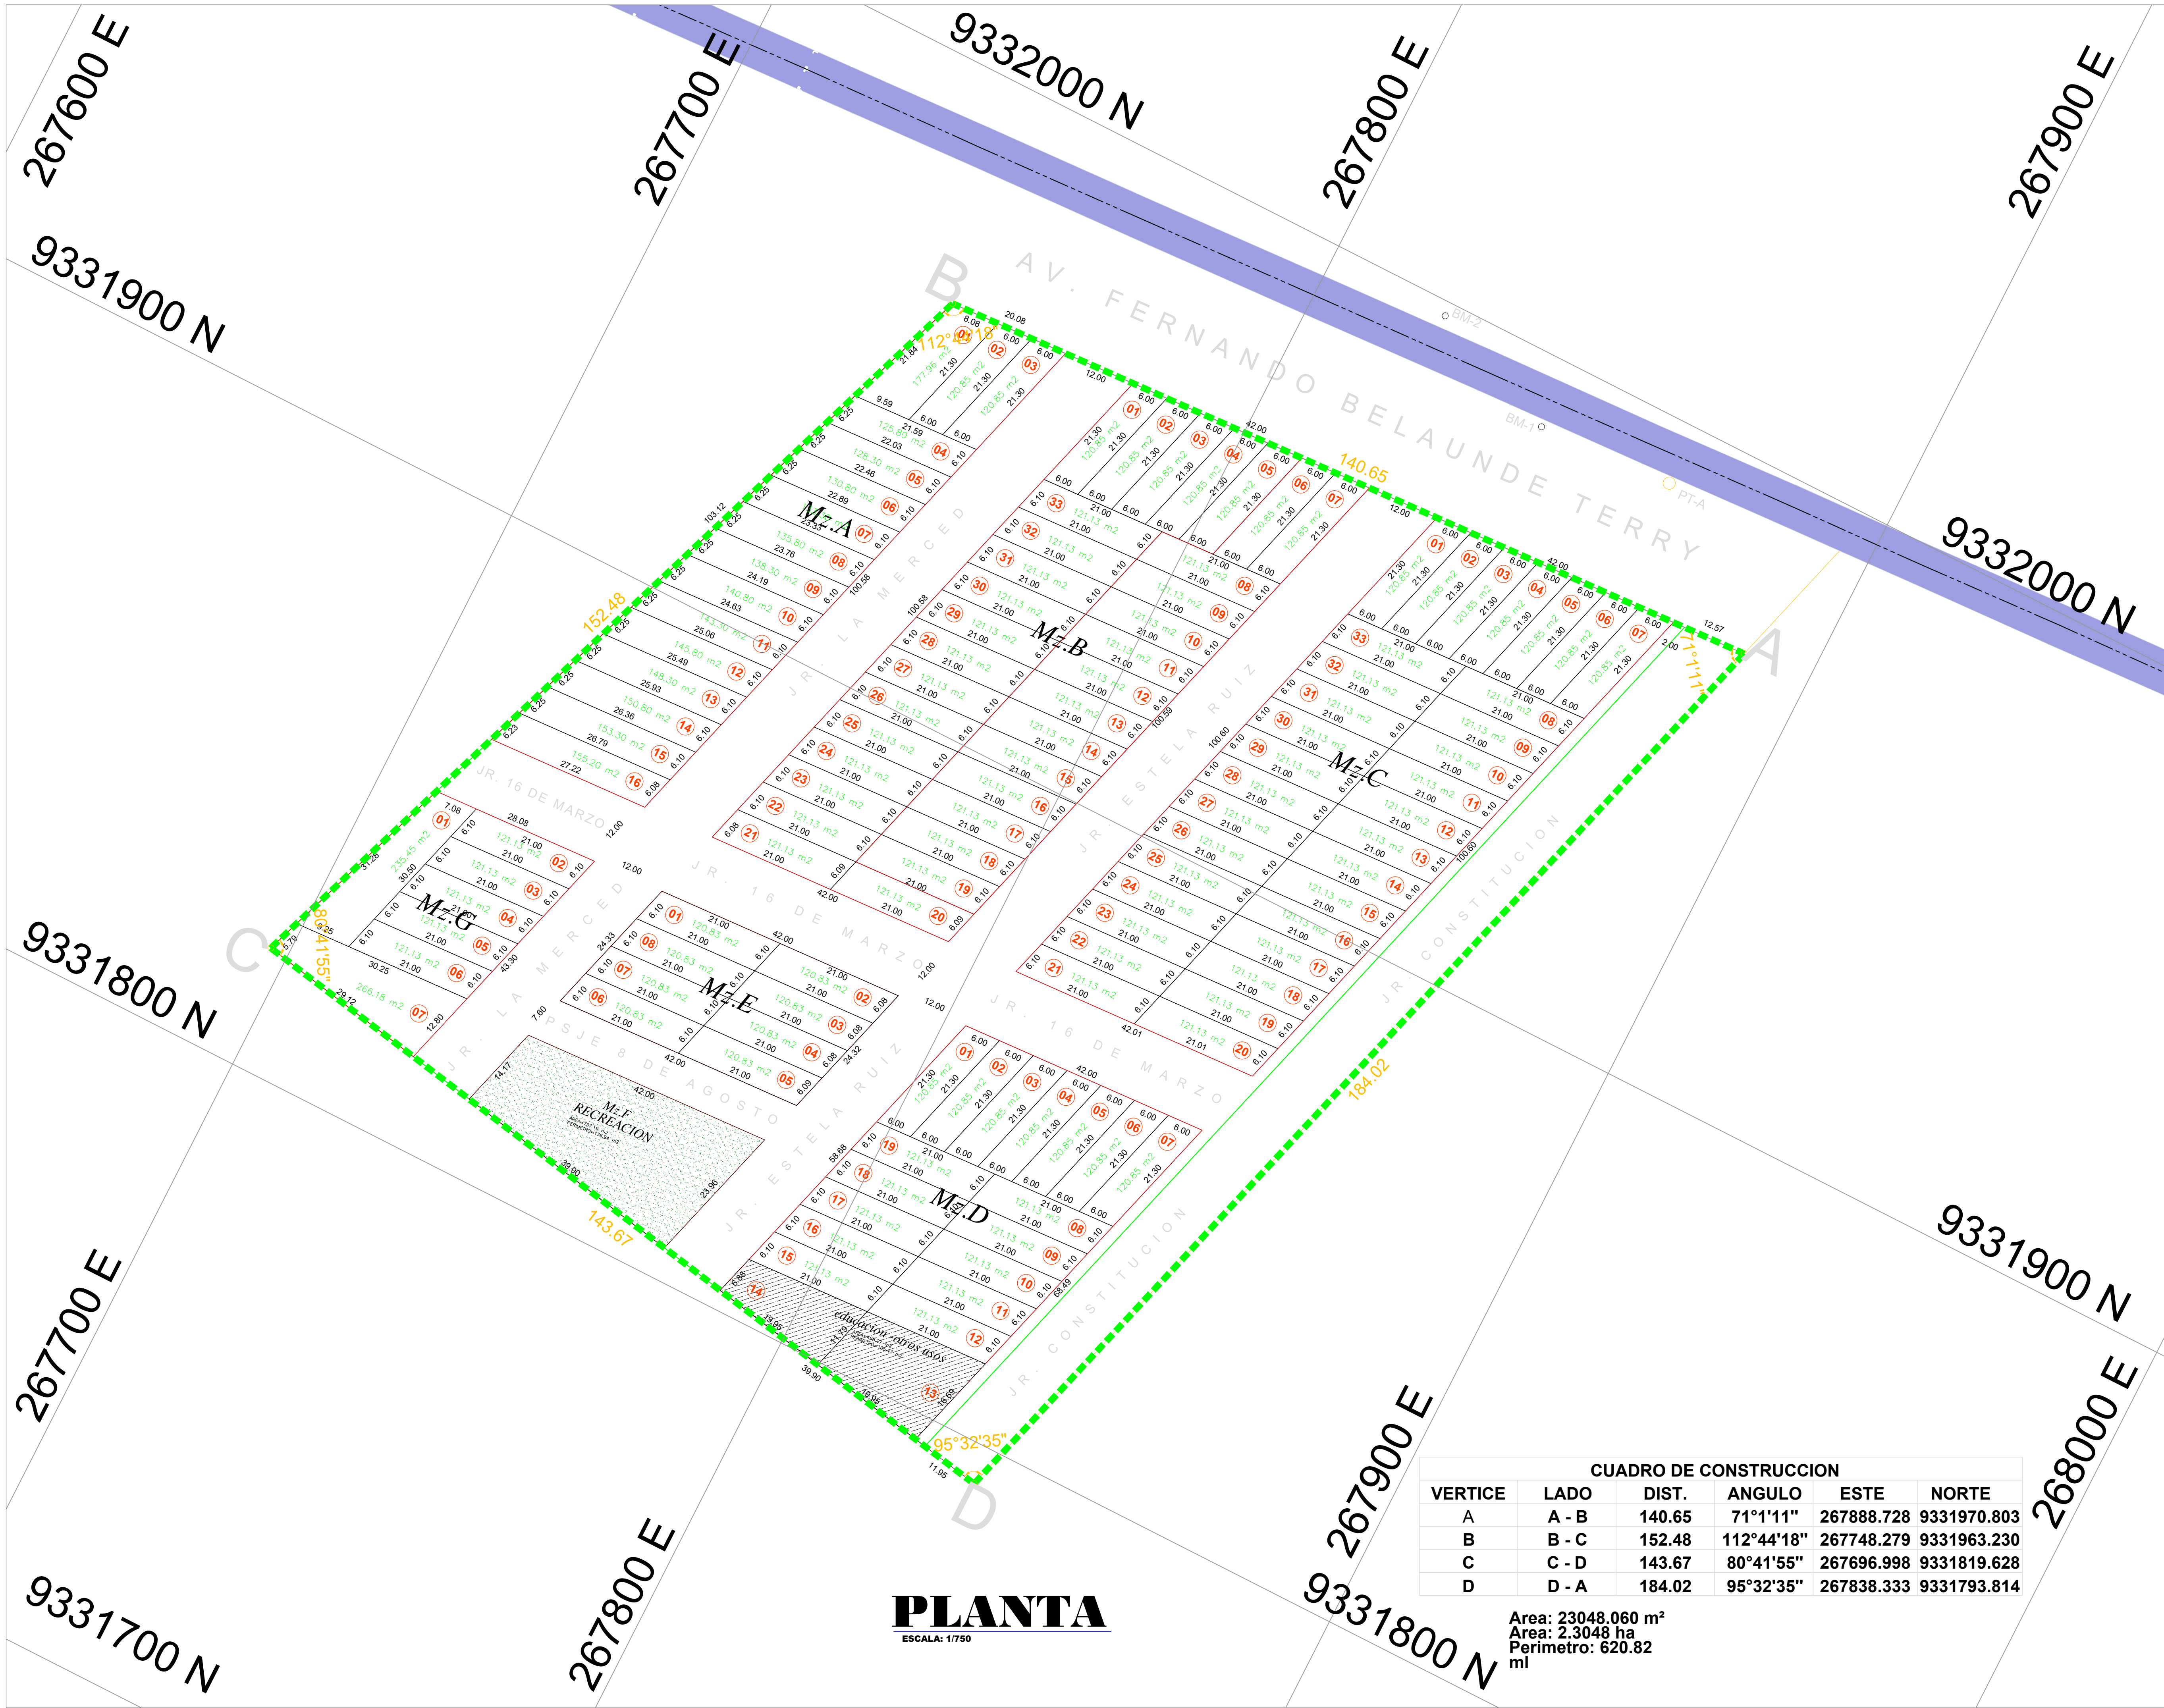

CUADRO DE CONSTRUCCION					
VERTICE	LADO	DIST.	ANGULO	ESTE	NORTE
A	A - B	140.65	71°1'11"	267888.728	9331970.803
B	B - C	152.48	112°44'18"	267748.279	9331963.230
C	C - D	143.67	80°41'55"	267696.998	9331819.628
D	D - A	184.02	95°32'35"	267838.333	9331793.814

Area: 23048.060 m²
Area: 2.3048 ha
Perimetro: 620.82 ml

PLANTA
ESCALA: 1/750



UBICACION DEL PROYECTO
ESCALA: 1/10,000

LEYENDA	
DESCRIPCION	SIMBOLO
E.L. DE VIA DISEÑADO	—
CAMINO EXISTENTE	- - -
PREDIO EXISTENTE	—
ACCESO EXISTENTE	- - -
CURVA MAYOR	—
CURVA MENOR	—
RIO Y QUEBRADAS	—
CARRETERA	—
PUENTE EXISTENTE	—
ALCANTARILLA EXISTENTE	—
PUNTOS DE CONTROL	—
BAL DEL PROYECTO	—
POSTE DE LUZ	—
POSTE DE TELEFONO	—
POSTE DE ALTA TENSION	—
POSTE DE MEDIA TENSION	—
BUDON DE DESAGUE	—
ARBOL	—

NOTAS:
- DATUM: WGS84
- ZONA: 18S
- GEODE: EDWARDS-1
- LAS COORDENADAS ESTAN EN EL SISTEMA UTM
- DIMENSIONES, ELEVACIONES Y COORDENADAS EN METROS.

LEYENDA	
TERRENO VIA EXISTENTE	—
CURVA SUBRASANTE	—
TANGENTE SUBRASANTE	—

PROYECTO:
URBANIZACION CON VENTA GARANTIZADA "LAS PALMERAS DE CALZADA"

PROPIETARIO:
**YEISON TAPIA SOPLA
YEFFERSON HOAN ESTELA RUIZ**

UBICACIÓN:
**SECTOR : CALZADA
DISTRITO : CALZADA
PROVINCIA : MOYOBAMBA
DEPARTAMENTO : SAN MARTIN**

EMPRESA RESPONSABLE:
**NERFAL MAQUINARIA&CONSTRUCCION SAC
RUC:20601394155**
ESTUDIO DE TOPOGRAFIA, CARRETERAS, CANALES, LOTIZACIONES, LEVANTAMIENTOS CATASTRALES, URBANO Y RURAL, GPS DIFERENCIAL, PUNTOS GEODESICOS DE ORDEN B Y C.

PLANO:
PLANO DE LOTIZACIÓN

EQUIPO TECNICO:
E. PEÑA F.
ESC: 1/500
FECHA: JULIO-2021

A-1