
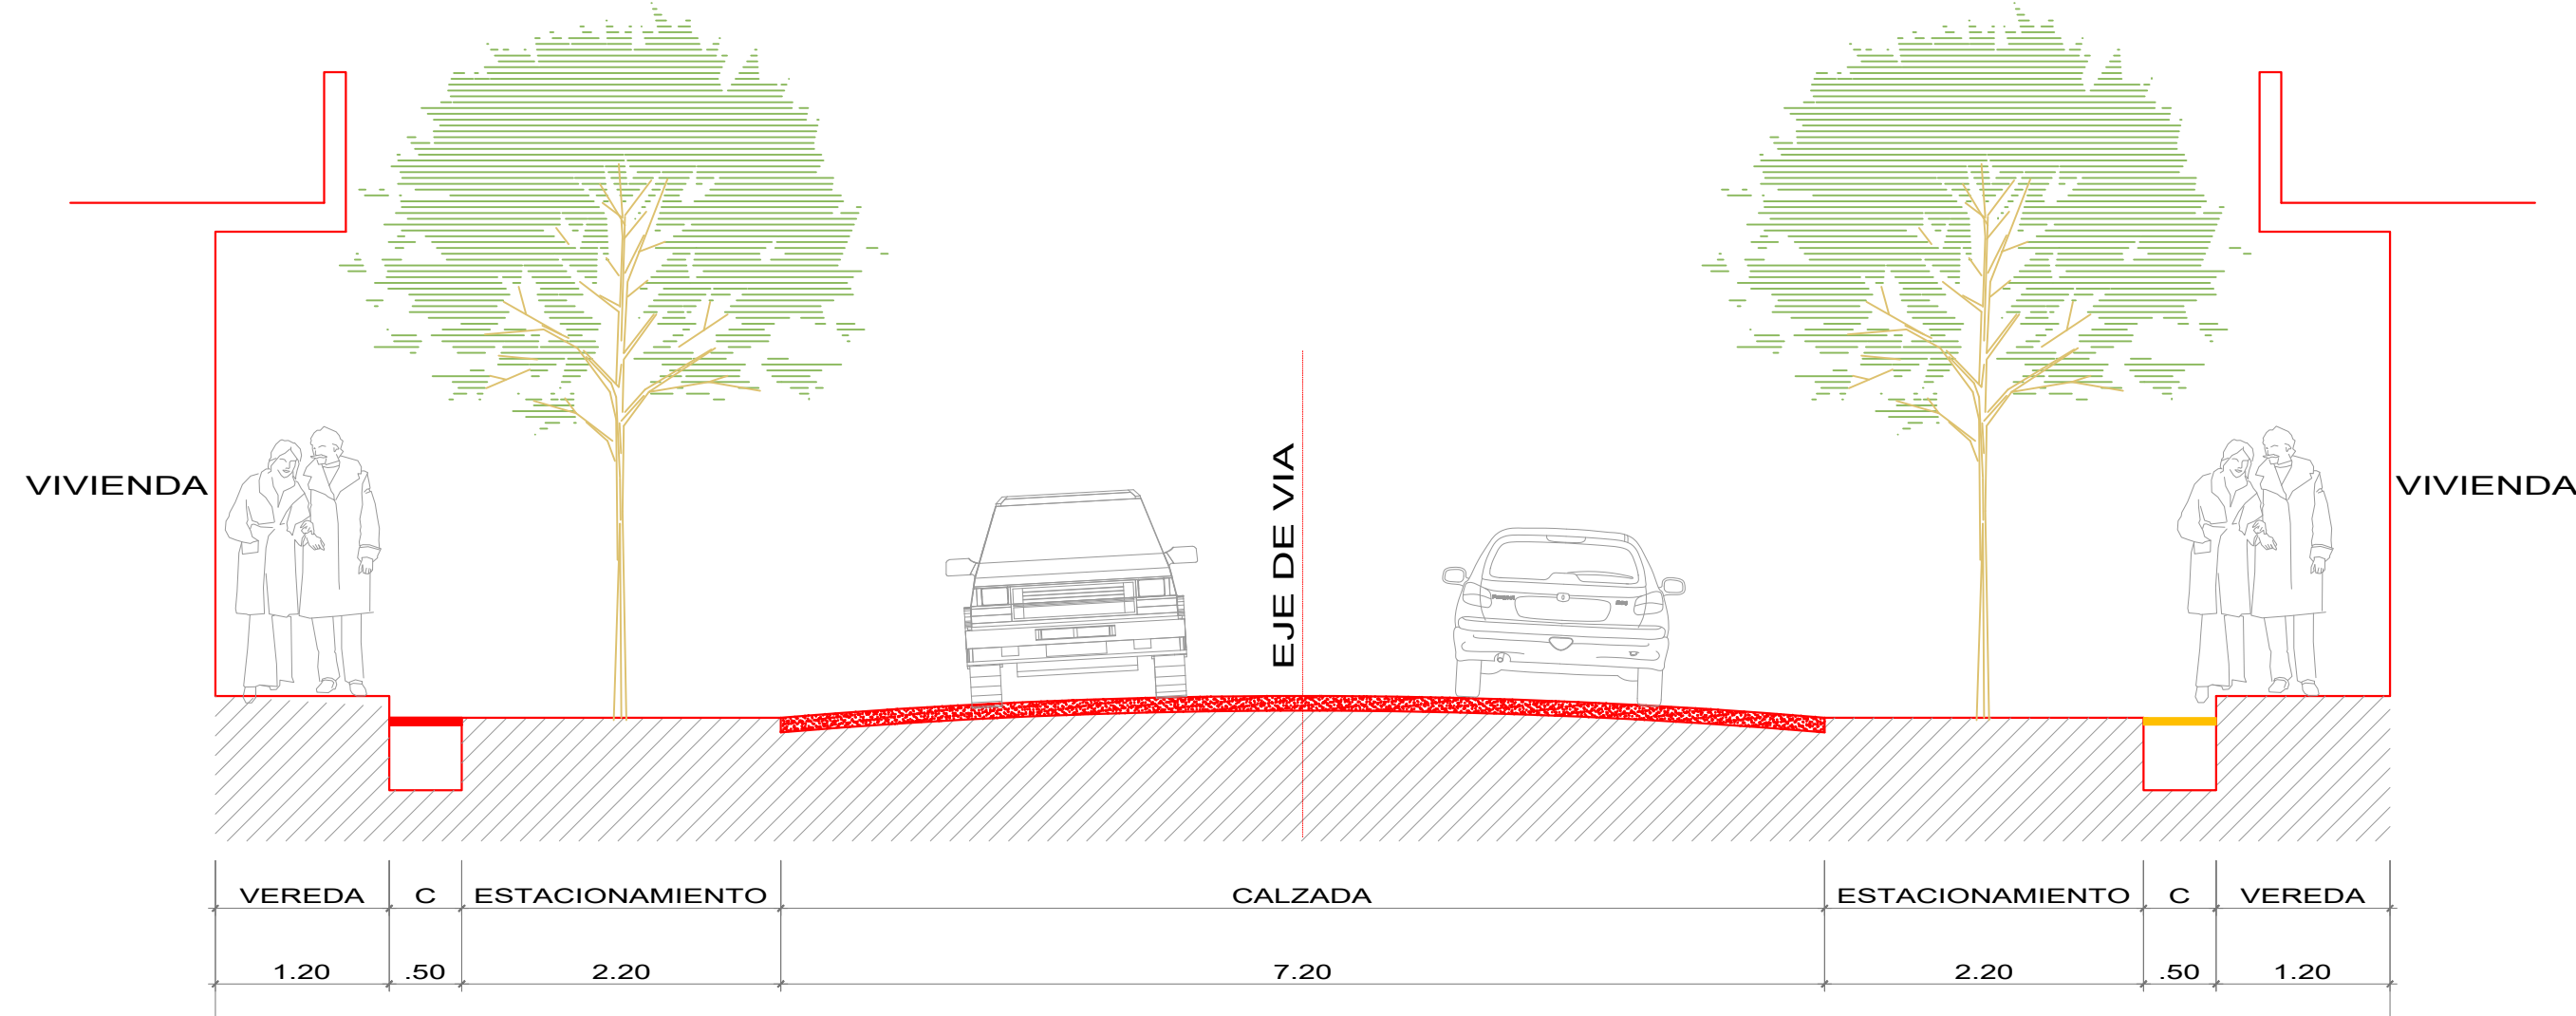
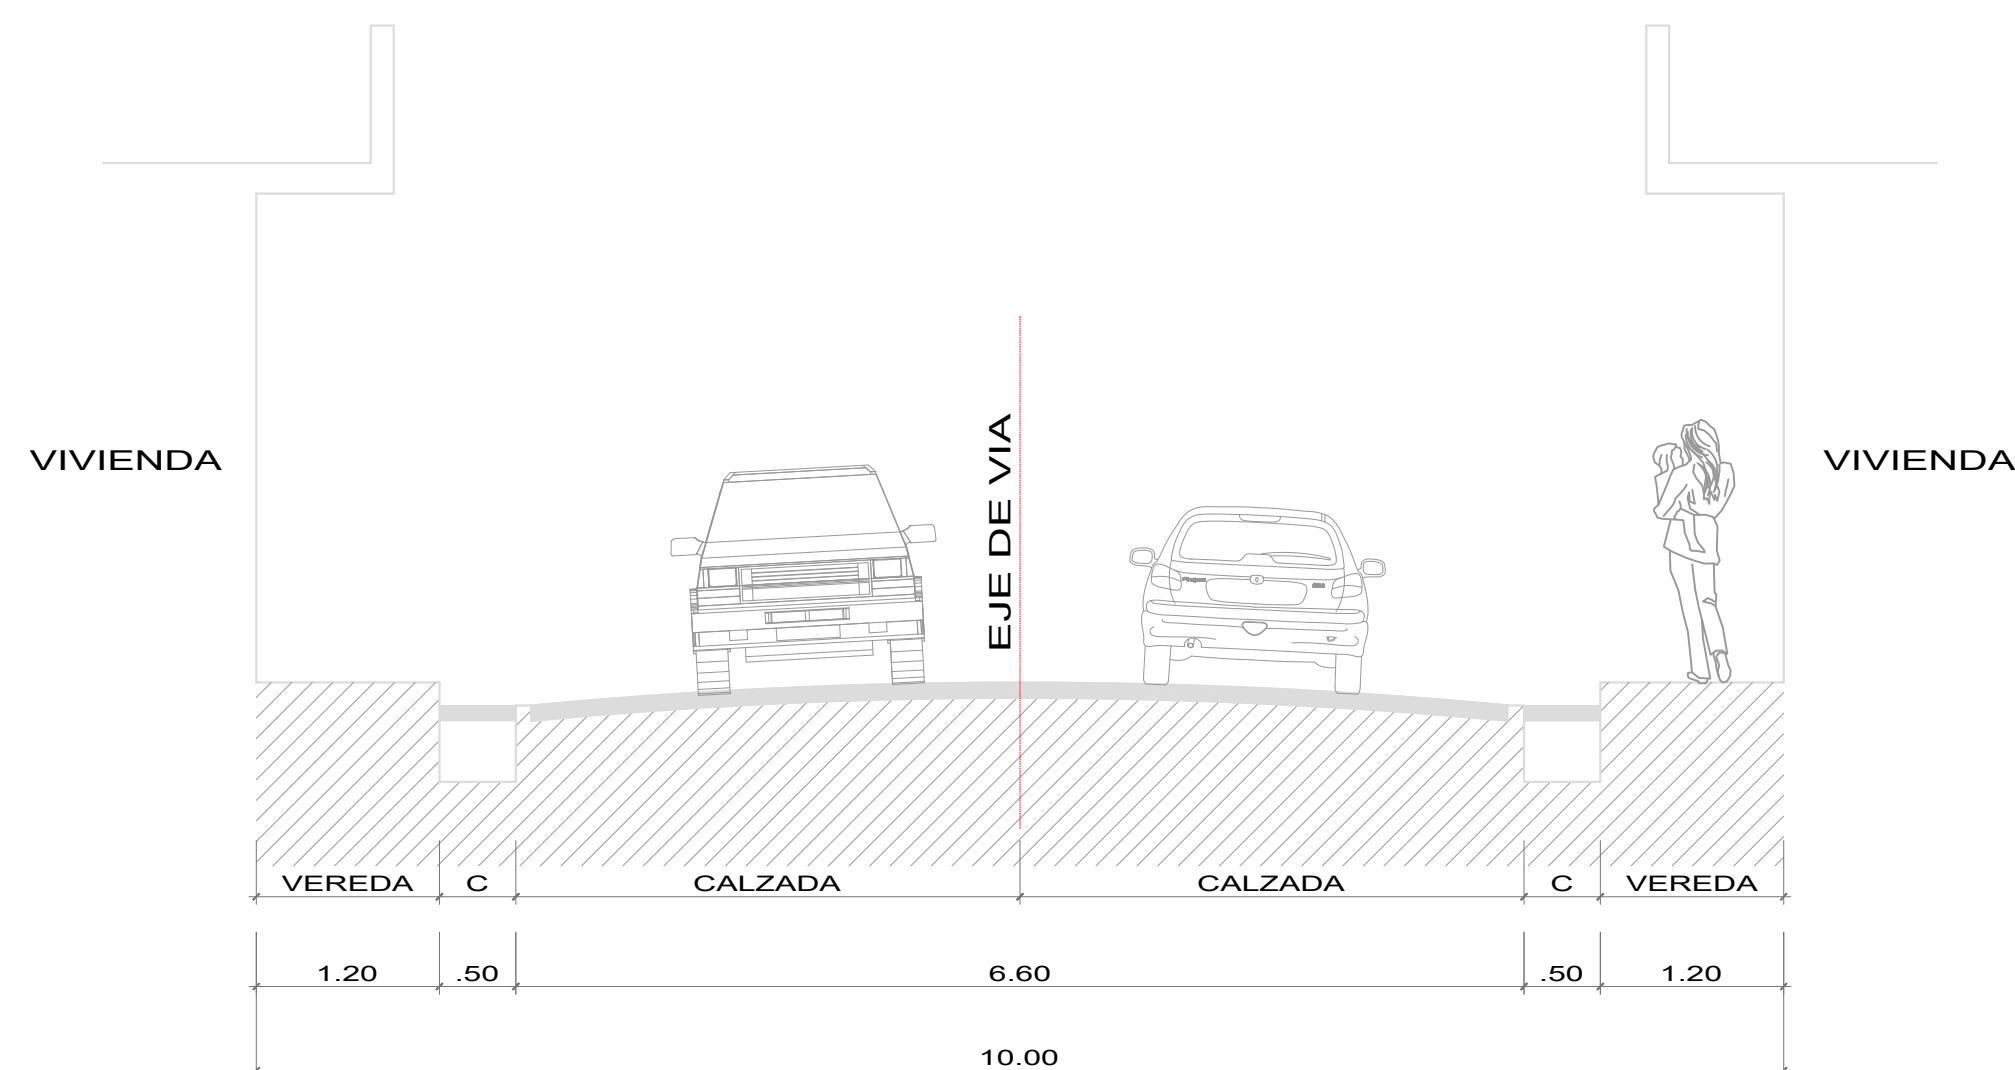


HABILITACION URBANA "MUNDO FELIZ" - LA UNIÓN

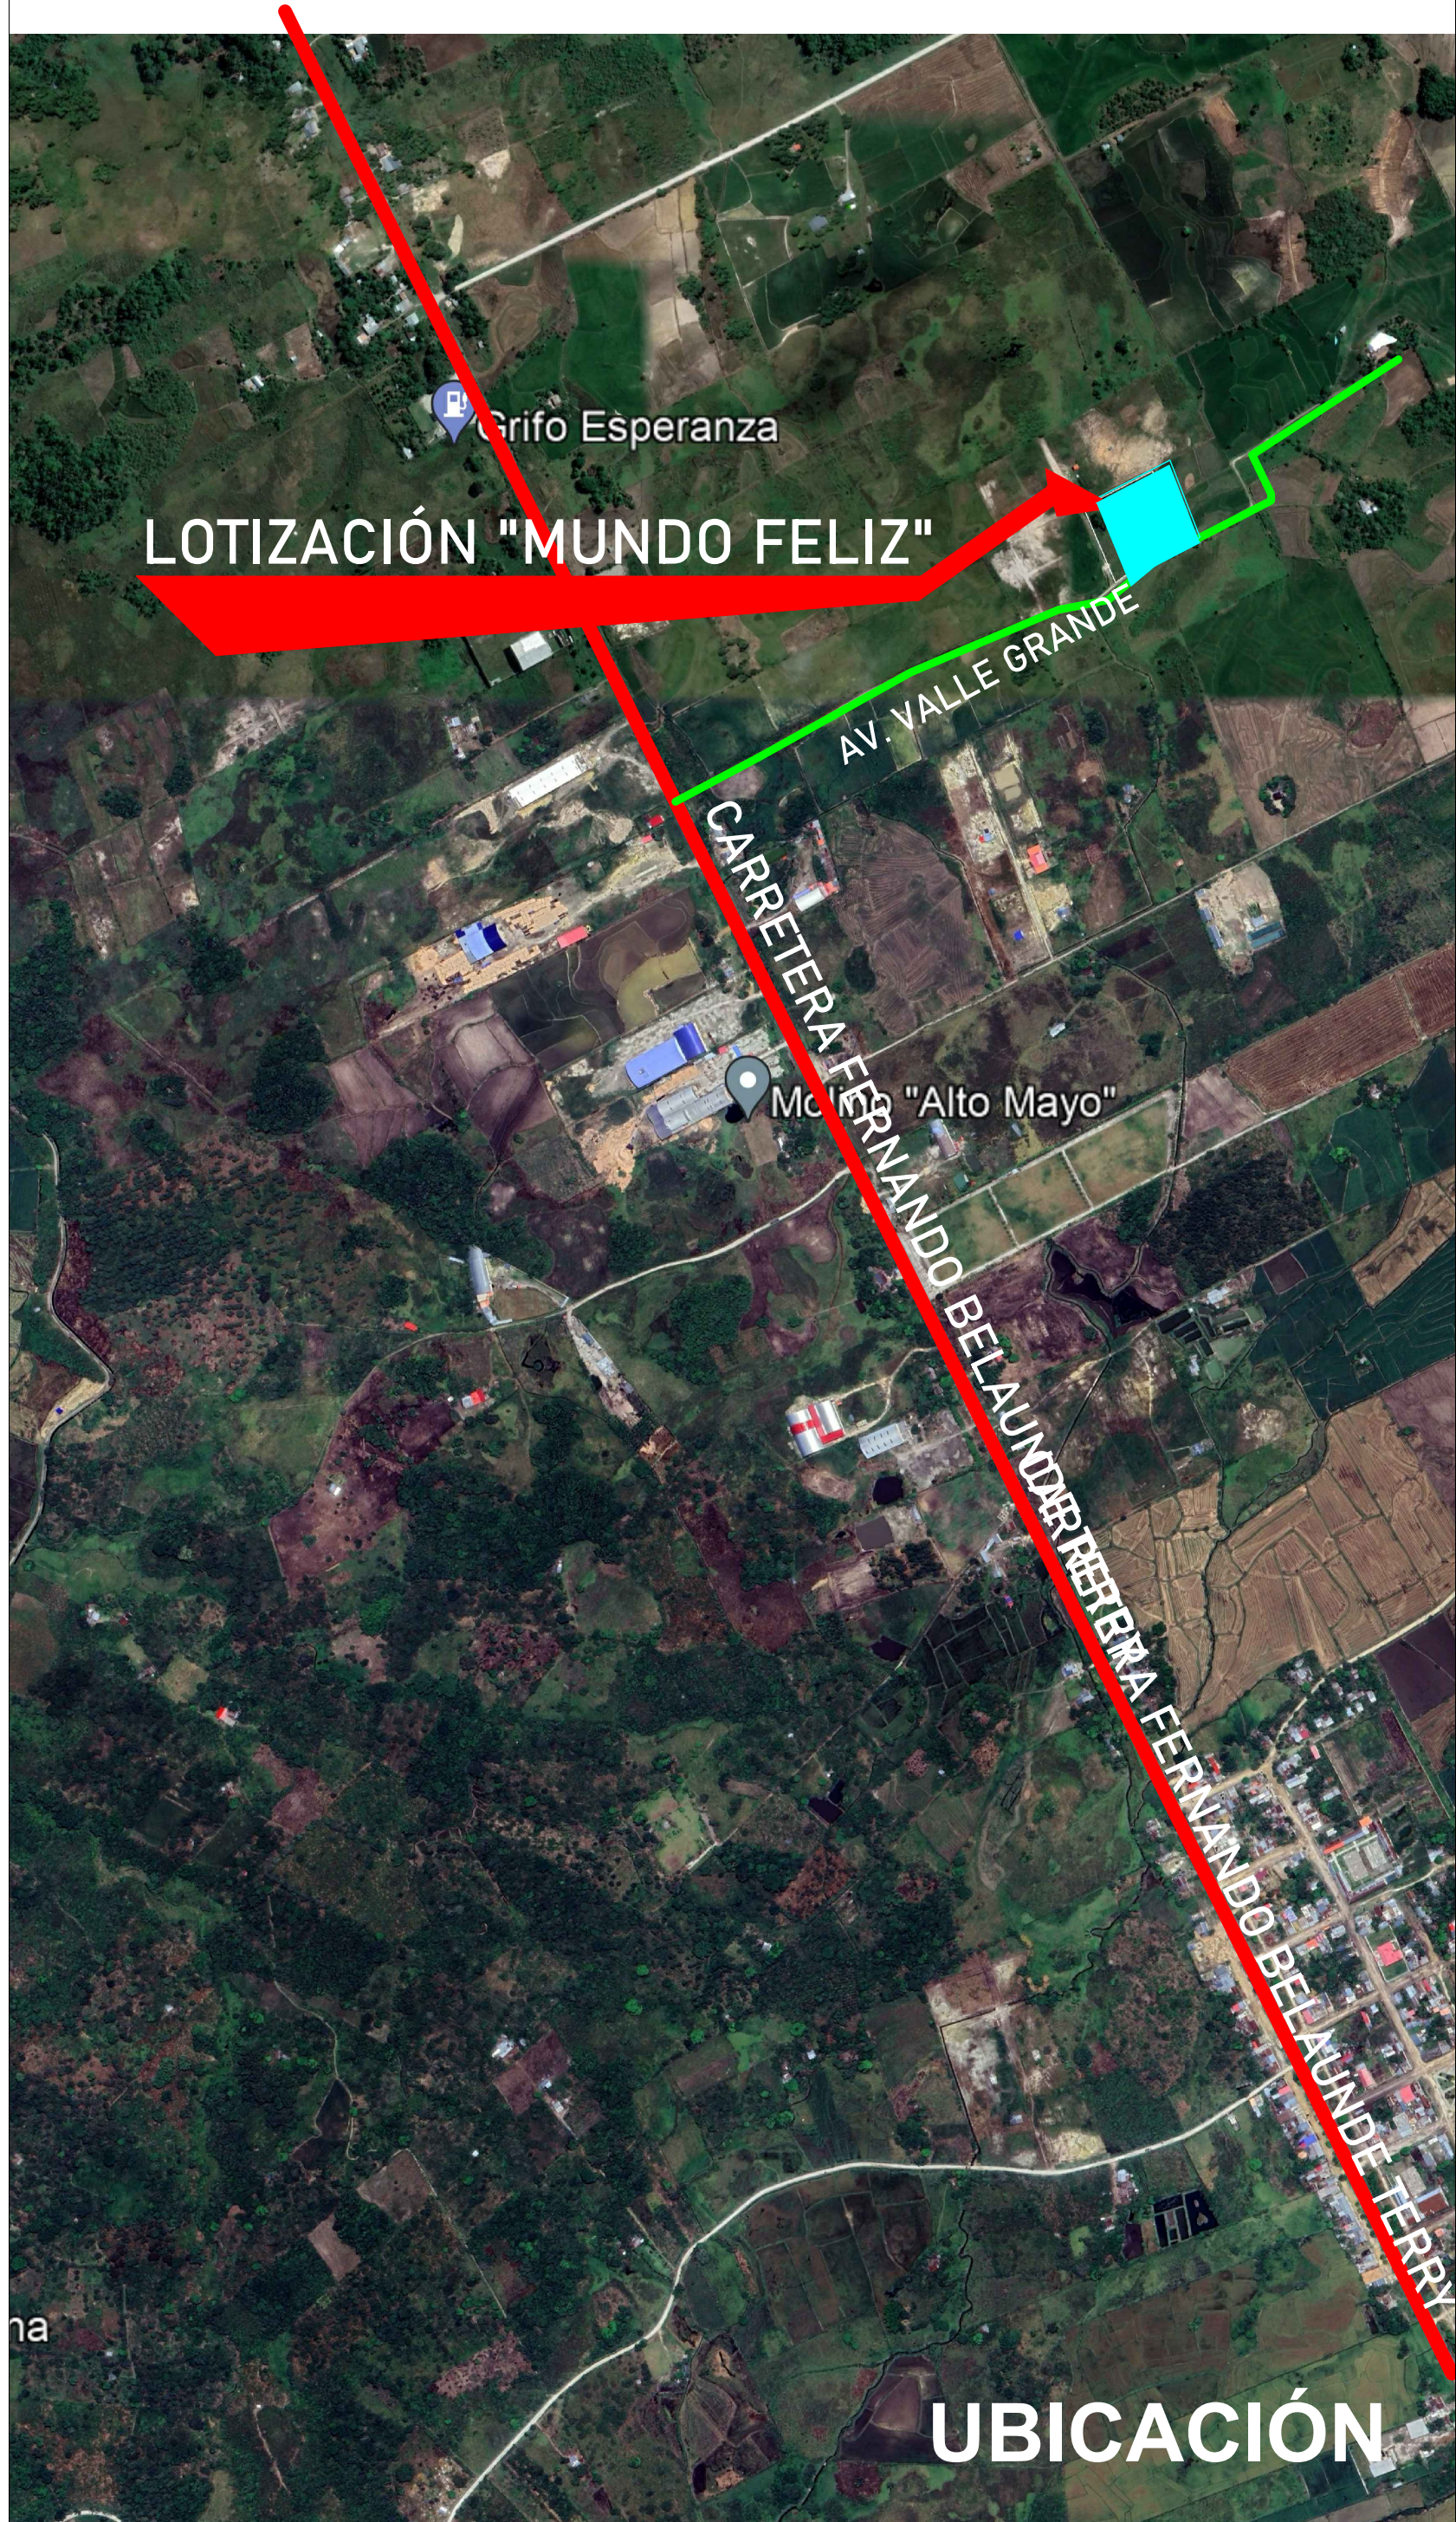

		PROYECTO: HABILITACION URBANA "MUNDO FELIZ"	
PROPIETARIO: OSMER COTRINA ACUÑA		PLANO: PLANO DE TRAZADO Y LOTIZACION	
SECTOR: SECTOR LA UNIÓN - NUEVA CAJAMARCA		UBICACION: SECTOR LA UNIÓN - NUEVA CAJAMARCA	
DISTRITO: NUEVA CAJAMARCA		PROVINCIA: RÍOJA	
REGION: SAN MARTIN		FECHA: 03/04/2023	
INSCRIPCION REGISTRAL: N° PARTIDA:		ESCALA: 1/750	
FIRMA DEL PROFESIONAL RESPONSABLE:		LAMINA: 01	